

Single-Story Detached Building
Southern Front
Section/Deep: 3:3 - *254cm*

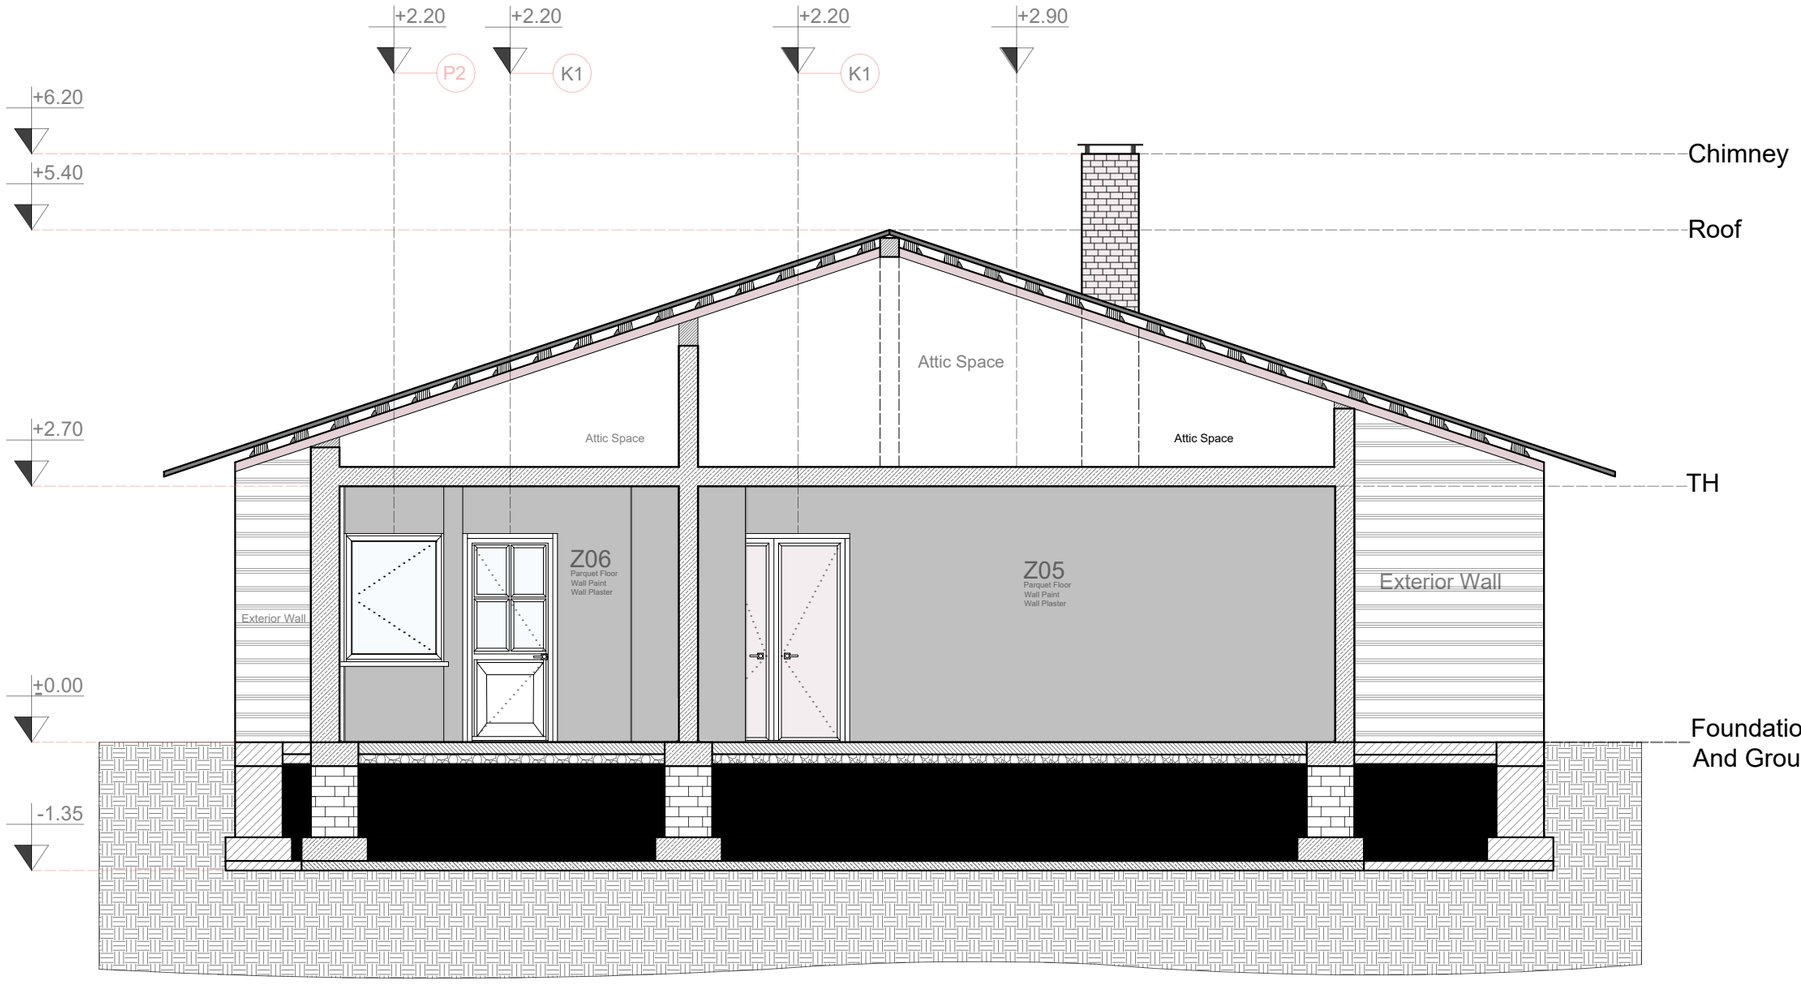

Section Part Dwg Guide

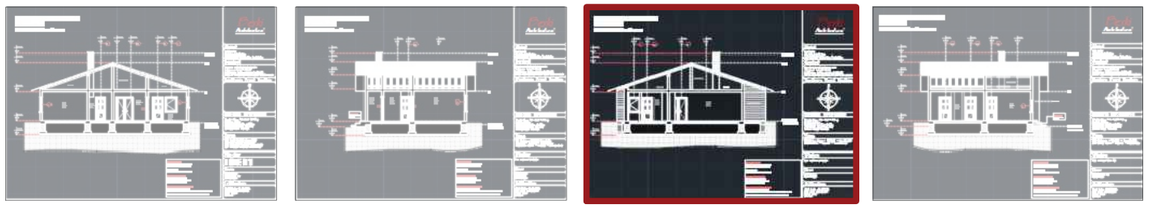

GROUND AREA
Floor Concrete Height: 10cm
Lean Concrete Height:13cm
Earth Ground
Level Concrete Height: 10cm

FOUNDATION AREA
Bond Beam: 25x25x50
Wall Foundation: 50x25x75
Foundation: 70x70x25

CHIMNEY AND ROOF AREA
50X60X50, Stone Veneer,
620 + 10cm (metal cover) High From The Entrance.
Pitched Roof, Top Cover Insulation Mat, Roofing,

Berki
Architectural


About

Sait Berki
44/Istanbul-Turkey
Architectural Restoration Technician

Contact

E-Mail: saitberkey@gmail.com
Telegram: t.me/saitberki
Instagram: instagram.com/saitberki
https://saitberki.github.io/Berki-Architectural

Southern Front Section

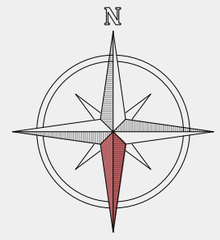

Building Information

Single-Story Detached Building
Height: 6.20m
Foundation Depth: -1.35m
Application Area: 131.045
Zoning Area: 146.796

Zone

Z05 Living Room - TH:2.70 - Area:31,983
Z06 Nursery - TH:2.70 - Area:16,916

Window

P2: 140X140-OKB 90

Door

K1:100X220
K3:160X220

3:3Section

Start Date: 16.10.2026
End Date: 22.10.2026
Page: 0005
Control: